


BUNK BED(1940X950X1800)
CODE:FP-BB-04-FO-FW-1.88


Q

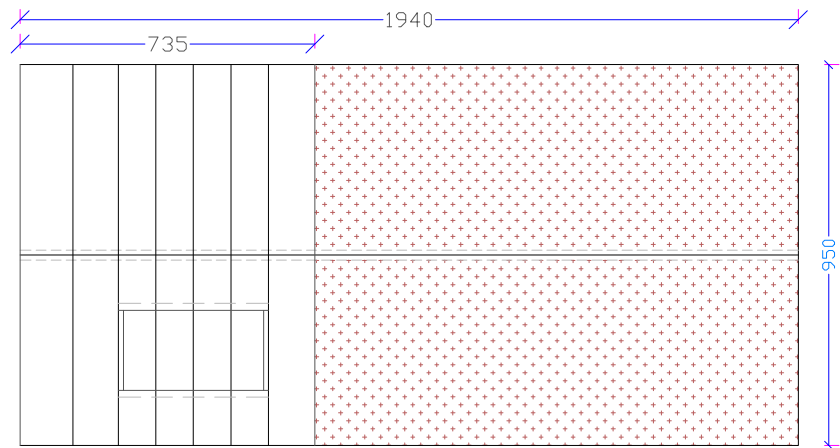


PLAN



REFERENCE IMAGE

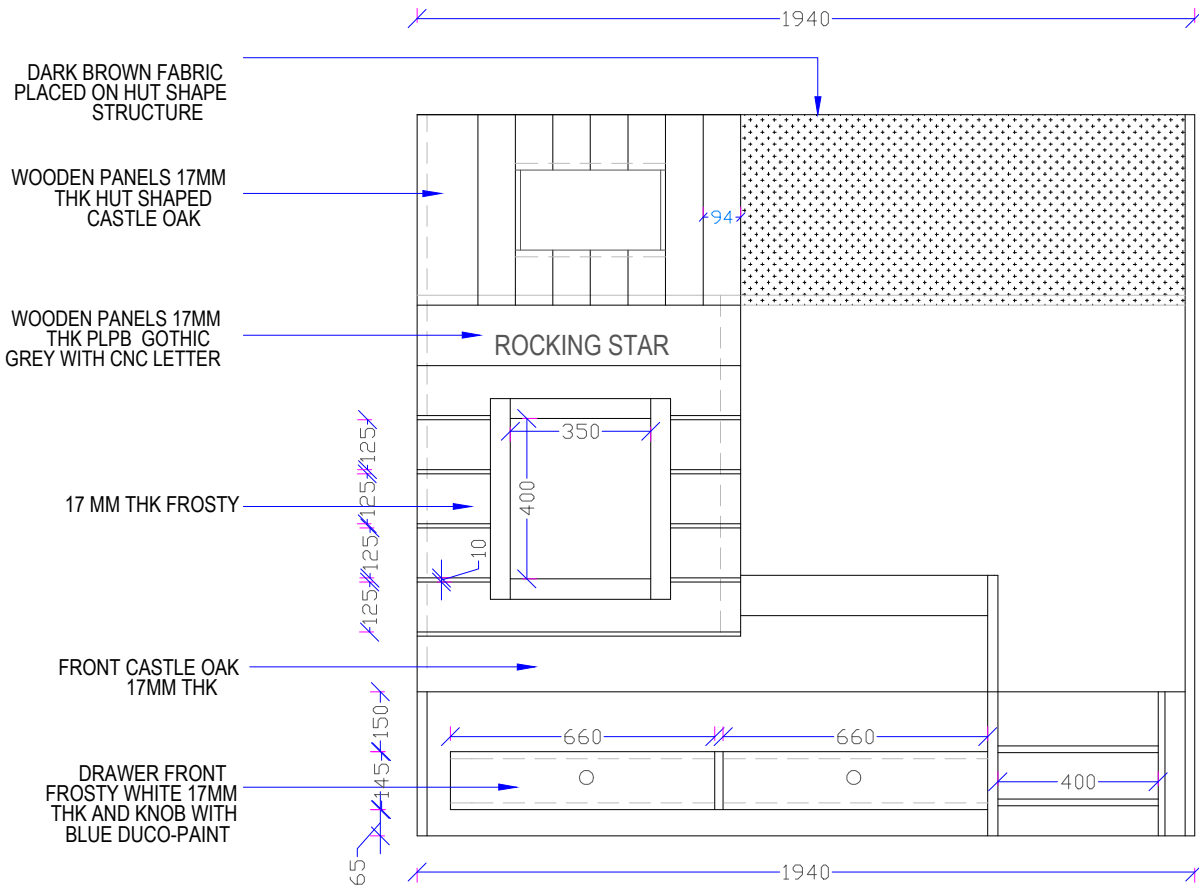

ELEVATION

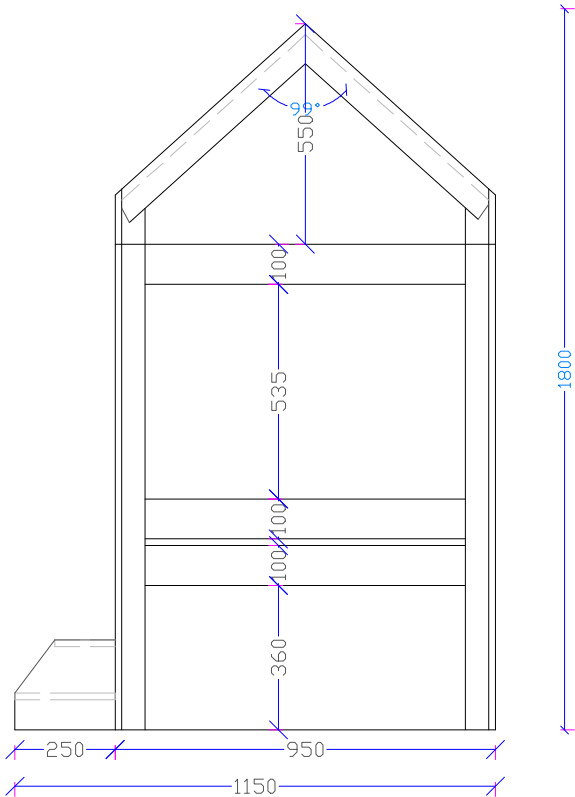

SIDE ELEVATION



SATYA INFRA PROMOTERS PVT. LTD.
KBC-3, THIRD FLOOR, SATYA ARCADE, ALAMBAGH, LUCKNOW, 226005.

General Notes:
Do not scale drawing.
Contractors shall verify all dimensions on site prior to construction.
All work shall be carried out in accordance with local authority regulations.
This drawing is copyright to satya infra promoter pvt ltd
Do not copy drawing without prior consent

NOTE:
1-MINIFIX + DOVEL USED FOR JOINERIES AND
BOARD EDGES ARE TREATED WITH PVC EDGE
BANDING.

CLIENT:

rev	date	notes
		First Issue

REVISIONS:

ISSUED FOR CONSTRUCTION
Resource Consent: N/A
Building Consent: N/A
Tender Issue: N/A
Construction Issue:

PROJECT:



DRAWING TITLE: BUNK BED		
SCALE: N.T.S.		
DRAWN BY: RANI		CHECKED:
PRINT DATE: 13/07/2022		PAGE
PROJECT No.	REVISION	SHEET No.
	R0	

BUNK BED(1940X950X1800)
CODE:FP-BB-04-FO-FW-1.88

Q

General Notes:
Do not scale drawing.
Contractors shall verify all dimensions on site prior to construction.
All work shall be carried out in accordance with local authority regulations.
This drawing is copyright to satya infra promoter pvt ltd
Do not copy drawing without prior consent

NOTE:
1-MINIFIX + DOVEL USED FOR JOINERIES AND
BOARD EDGES ARE TREATED WITH PVC EDGE
BANDING.

CLIENT:


		First Issue
rev	date	notes

REVISIONS:

ISSUED FOR CONSTRUCTION
Resource Consent: N/A
Building Consent: N/A
Tender Issue: N/A
Construction Issue:


PROJECT:

DRAWING TITLE: BUNK BED		
SCALE: N.T.S.		
DRAWN BY: RANI		CHECKED:
PRINT DATE: 13/07/2022	PAGE	
PROJECT No.	REVISION	SHEET No.
	R0	

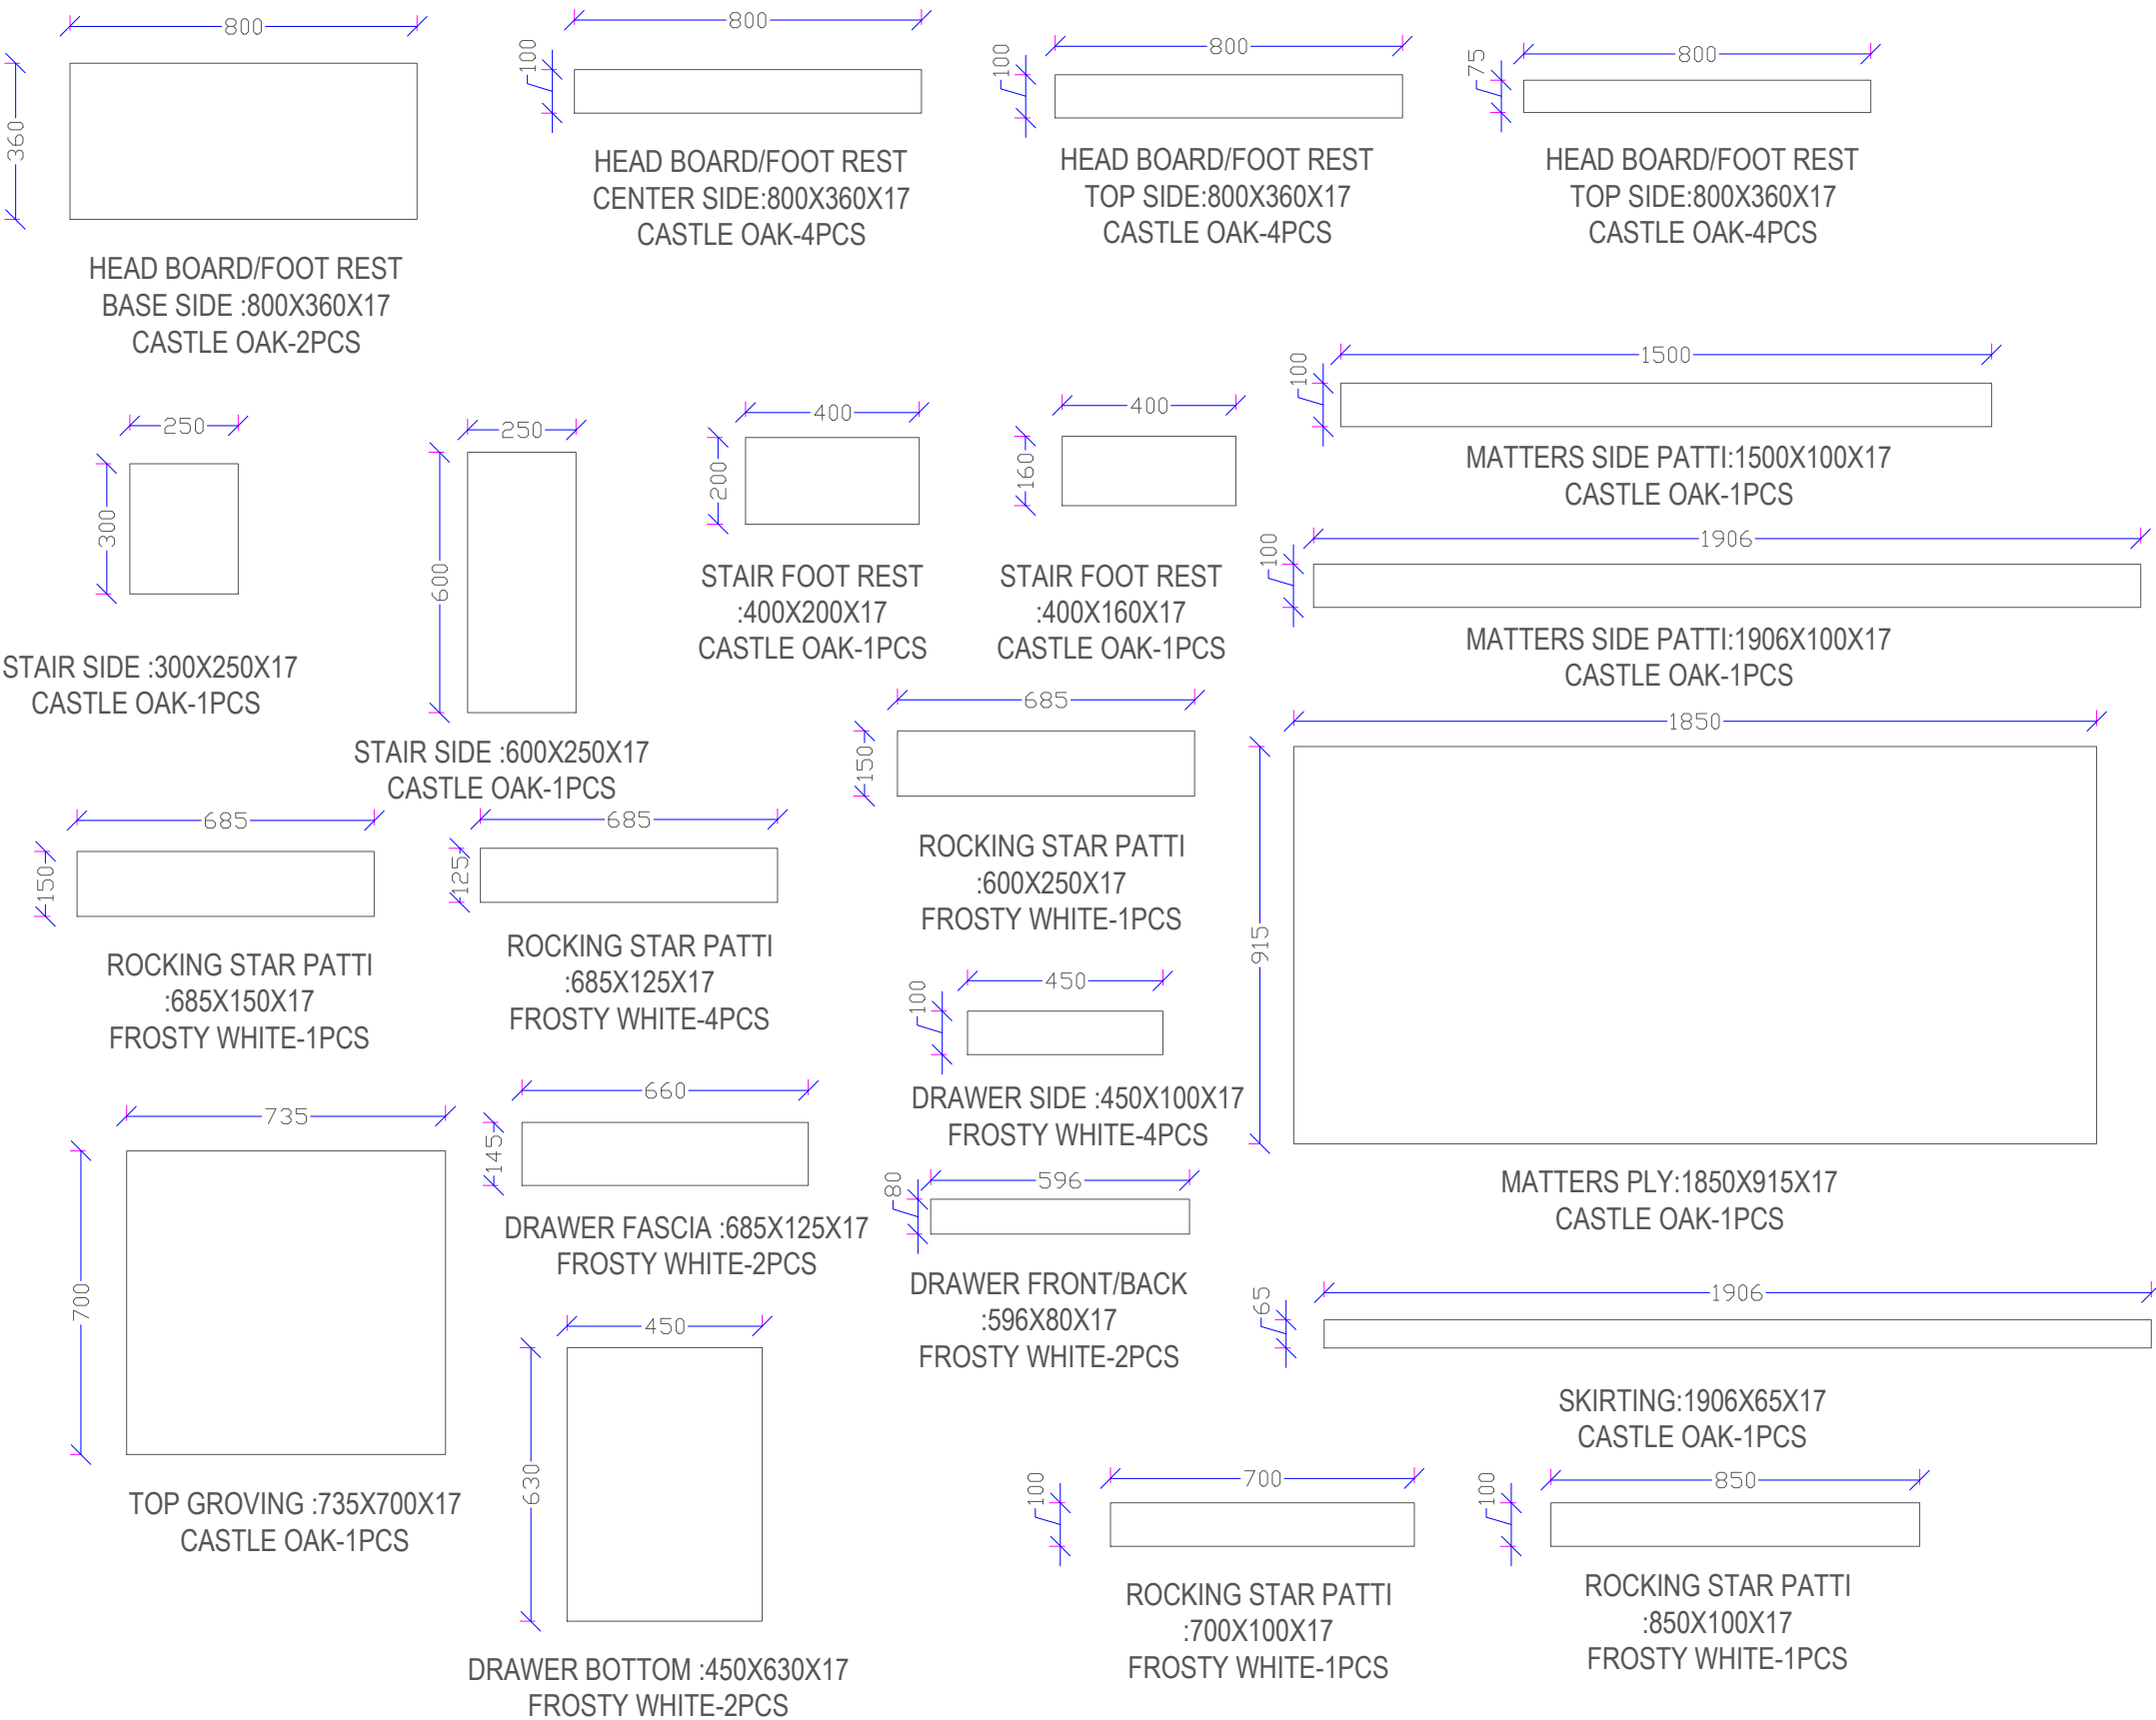

DISPLAY TABLE (755X600X1350)


CODE: FP-DT-11-FO-FW-0.75

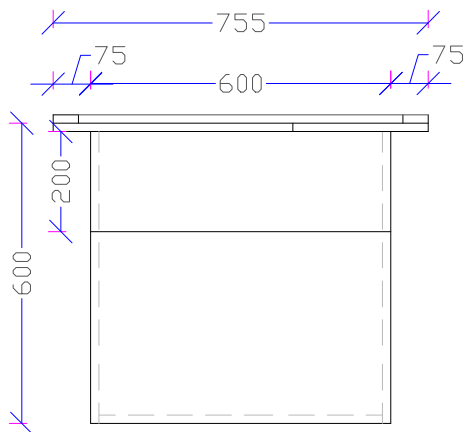


PLAN




REFERENCE IMAGE

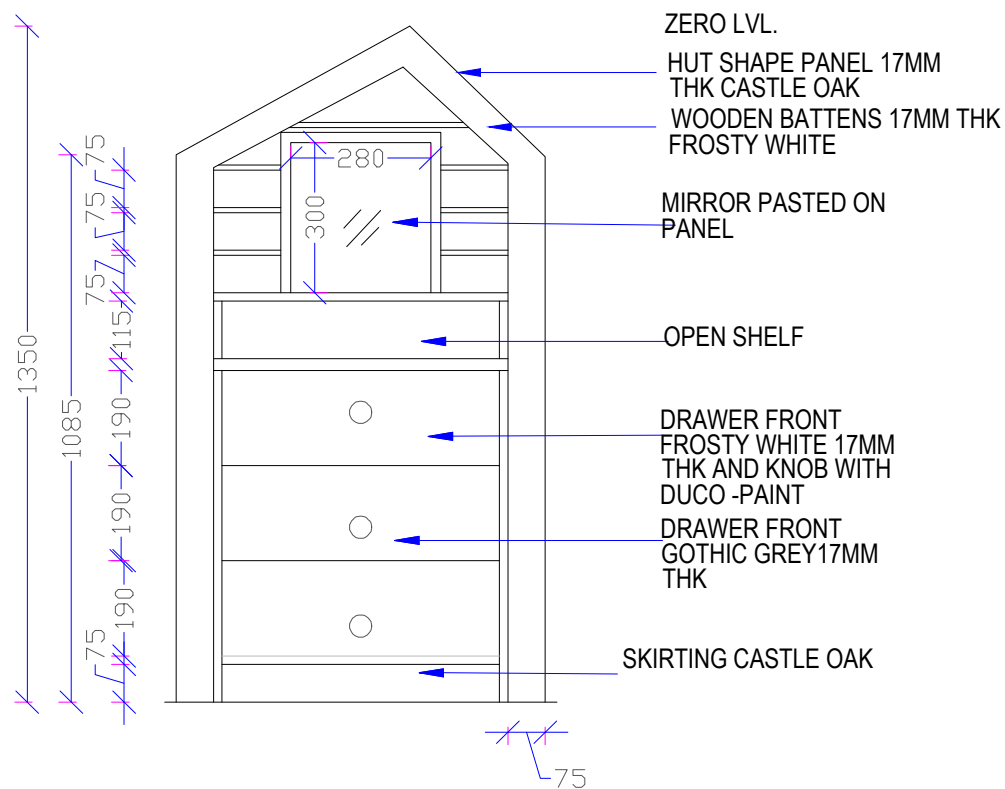

ELEVATION

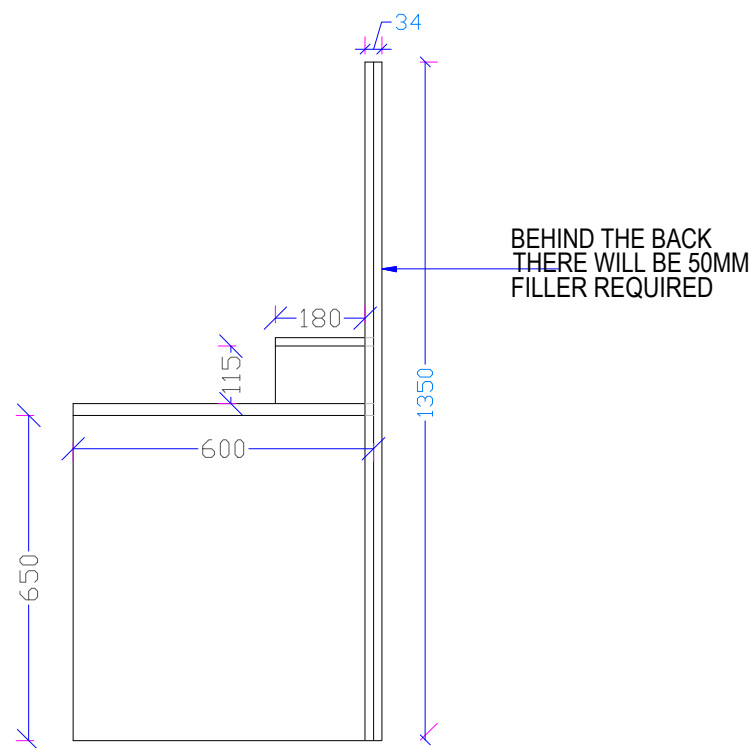

SIDE ELEVATION

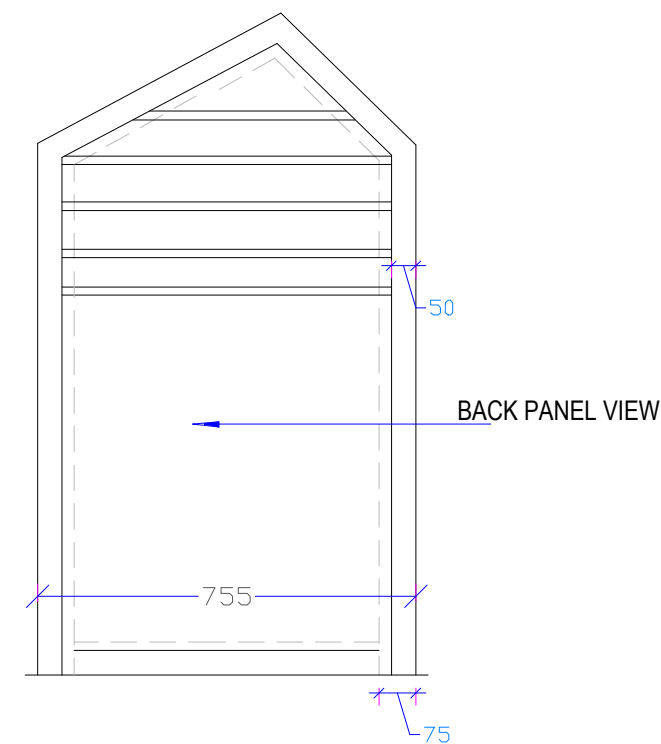

BACK ELEVATION



SATYA INFRA PROMOTERS PVT. LTD.
KBC-3, THIRD FLOOR, SATYA ARCADE, ALAMBAGH, LUCKNOW. 226005.

<p>General Notes:</p> <p>Do not scale drawing.</p> <p>Contractors shall verify all dimensions on site prior to construction.</p> <p>All work shall be carried out in accordance with local authority regulations.</p> <p>This drawing is copyright to satya infra promoter pvt ltd</p> <p>Do not copy drawing without prior consent</p>

NOTE:
1-MINIFIX + DOVEL USED FOR JOINERIES AND
BOARD EDGES ARE TREATED WITH PVC EDGE
BANDING.

CLIENT:

		First issue
rev	date	notes

REVISIONS:

ISSUED FOR CONSTRUCTION

Resource Consent: N/A

Building Consent:	N/A
-------------------	-----

Tender Issue:	N/A
---------------	-----

Construction Issue:

PROJECT:



DRAWING TITLE:

DISPLAY TABLE

SCALE:	N.T.S.
--------	--------

DRAWN BY: RANI	CHECKED:
----------------	----------

PRINT DATE: 13/07/2022	PAGE
------------------------	------

PROJECT No.	REVISION	SHEET No.
-------------	----------	-----------

DISPLAY TABLE (755X600X1350)
CODE: **FP-DT-11-FO-FW-0.75**

Q1

General Notes:
Do not scale drawing.
Contractors shall verify all dimensions on site prior to construction.
All work shall be carried out in accordance with local authority regulations.
This drawing is copyright to satya infra promoter pvt ltd
Do not copy drawing without prior consent

NOTE:
1-MINIFIX + DOVEL USED FOR JOINERIES AND
BOARD EDGES ARE TREATED WITH PVC EDGE
BANDING.

CLIENT:


rev	date	notes
		First Issue

REVISIONS:


ISSUED FOR CONSTRUCTION
Resource Consent: N/A
Building Consent: N/A
Tender Issue: N/A
Construction Issue:

PROJECT:


DRAWING TITLE: DISPLAY TABLE		
SCALE: N.T.S.		
DRAWN BY: RANI		CHECKED:
PRINT DATE: 13/07/2022	PAGE	
PROJECT No.	REVISION	SHEET No.
	R0	

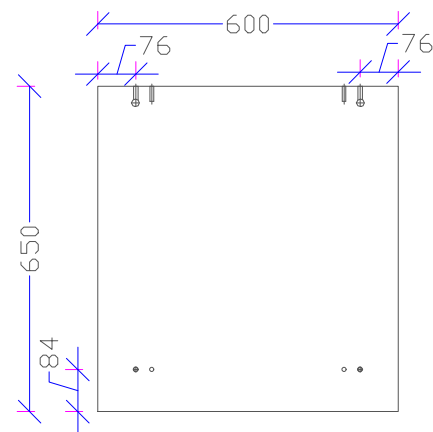


SIDE LEG:600X650X17
CASTLE OAK-2PCS

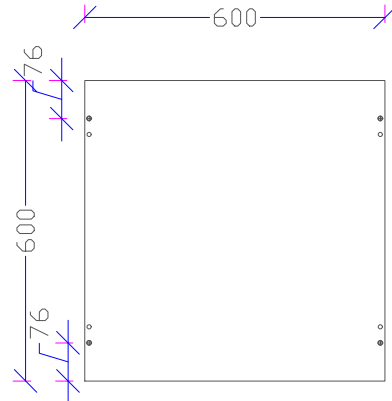


TOP PANEL:600X600X25
CASTLE OAK-1PCS

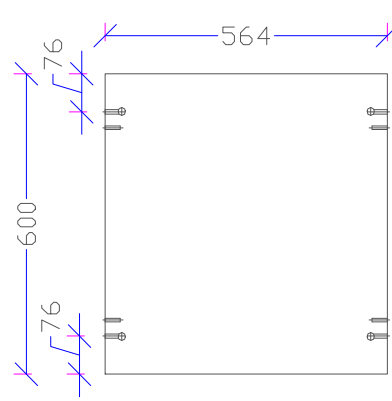


BOTTOM PANEL:564X600X17
FROSTY WHITE-1PCS

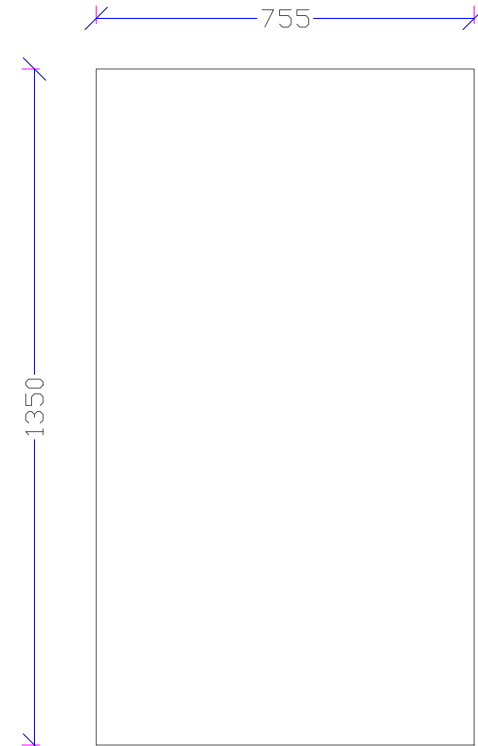


BACK:755X1350X17
FROSTY WHITE-1PCS

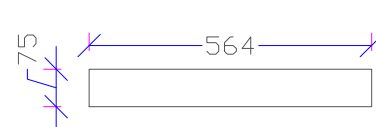


SKIRTING:564X75X17
CASTLE OAK-1PCS

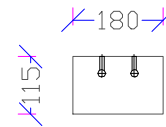


SIDE:180X115X17
CASTLE OAK-2PCS

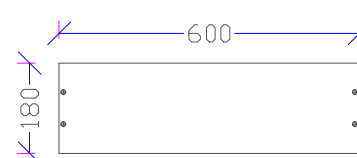


TOP:600X180X17
CASTLE OAK-1PCS

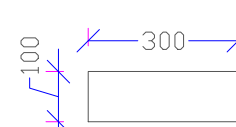


MIRROR SIDE:600X180X17
CASTLE OAK-1PCS

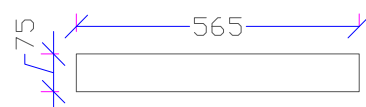

MIRROR SIDE TOP:565X75X17
CASTLE OAK-1PCS

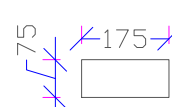


MIRROR SIDE PATTI:175X75X17
CASTLE OAK-1PCS

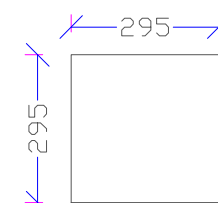


MIRROR BACK PLY:295X295X17
CASTLE OAK-1PCS




DRAWER FASCIA:562X190X17
FROSTY WHITE-2PCS

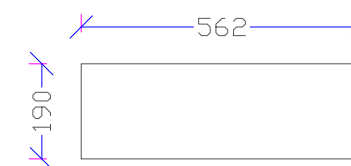


DRAWER FASCIA:562X190X17
GREY-1PCS

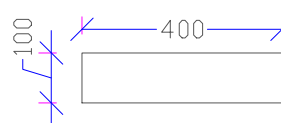

DRAWER SIDE :400X100X17
FROSTY WHITE-6PCS

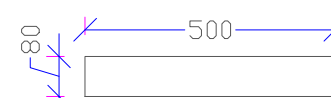

DRAWER FRONT/ BACK :400X100X17
FROSTY WHITE-6PCS

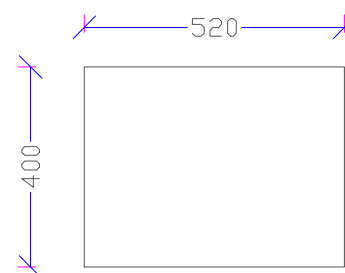

DRAWER BOTTOM :520X400X17
FROSTY WHITE-3PCS

WARDROBE (1220X650X1850)
CODE:FP-WRB-30-FO-FW-1.2

Q2



REFERENCE IMAGE

General Notes:
Do not scale drawing.
Contractors shall verify all dimensions on site prior to construction.
All work shall be carried out in accordance with local authority regulations.
This drawing is copyright to satya infra promoter pvt ltd
Do not copy drawing without prior consent

NOTE:
1-MINIFIX + DOVEL USED FOR JOINERIES AND
BOARD EDGES ARE TREATED WITH PVC EDGE
BANDING.

CLIENT:


rev	date	notes
		First Issue

REVISIONS:


ISSUED FOR CONSTRUCTION
Resource Consent: N/A
Building Consent: N/A
Tender Issue: N/A
Construction Issue:

PROJECT:

DRAWING TITLE: WARDROBE		
SCALE: N.T.S.		
DRAWN BY: RANI		CHECKED:
PRINT DATE: 13/07/2022		PAGE
PROJECT No.	REVISION	SHEET No.
	R0	

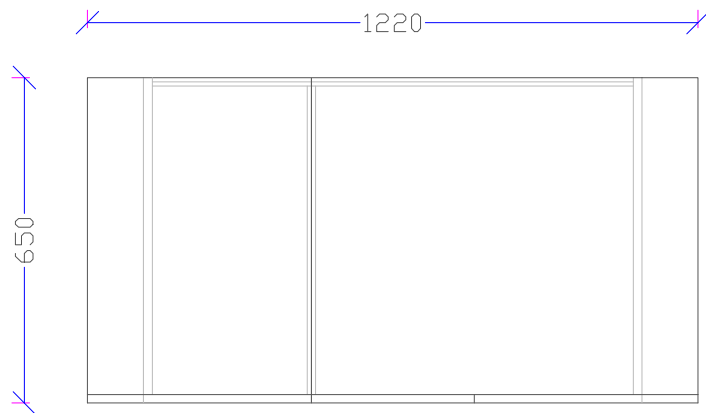


PLAN

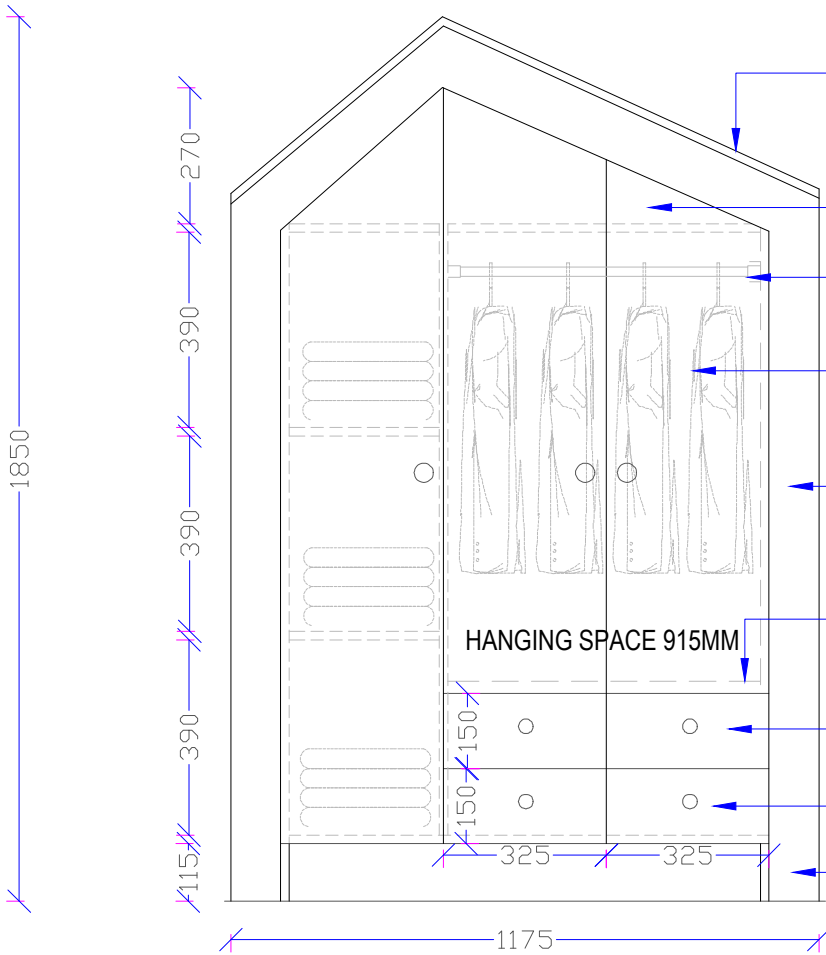

ELEVATION

- HUT SHAPE PANEL 17MM THK CASTLE OAK
- FRONT 17MM THK CASTLE OAK
- HANGING ROD
- SHUTTER 17MM THK FROSTY WHITE
- FILLER WILL BE DONE ON CNC MACHINE ONLY FRONT SIDE
- ALL SHELF 25MM THK FROSTY WHITE
- DRAWER 17MM THK PERSIAN BLUE
- DRAWER 17MM THK GOTHIC GREY
- FRONT CASTLE OAK

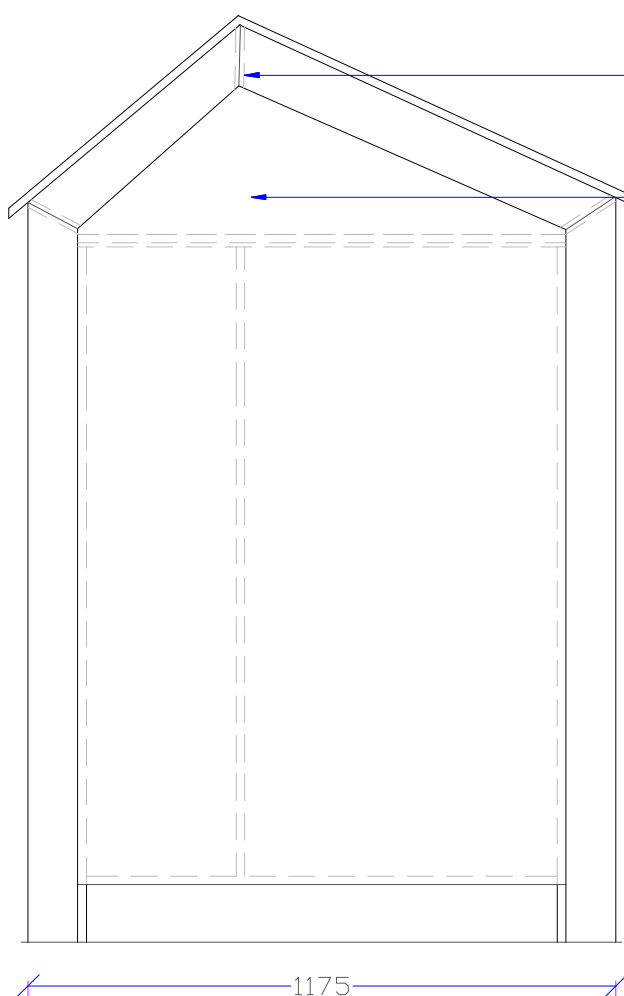

BACK ELEVATION

- 17MM THK FROSTY WHITE SUPPORT
- BACK COVER PANEL 17MM THK FROSTY WHITE

WARDROBE (1220X650X1850)

CODE:FP-WRB-30-FO-FW-1.2


Q2



SATYA INFRA PROMOTERS PVT. LTD.
KBC-3, THIRD FLOOR, SATYA ARCADE, ALAMBAGH, LUCKNOW, 226005.

General Notes:
Do not scale drawing.
Contractors shall verify all dimensions on site prior to construction.
All work shall be carried out in accordance with local authority regulations.
This drawing is copyright to satya infra promoter pvt ltd
Do not copy drawing without prior consent

NOTE:
1-MINIFIX + DOVEL USED FOR JOINERIES AND
BOARD EDGES ARE TREATED WITH PVC EDGE
BANDING.

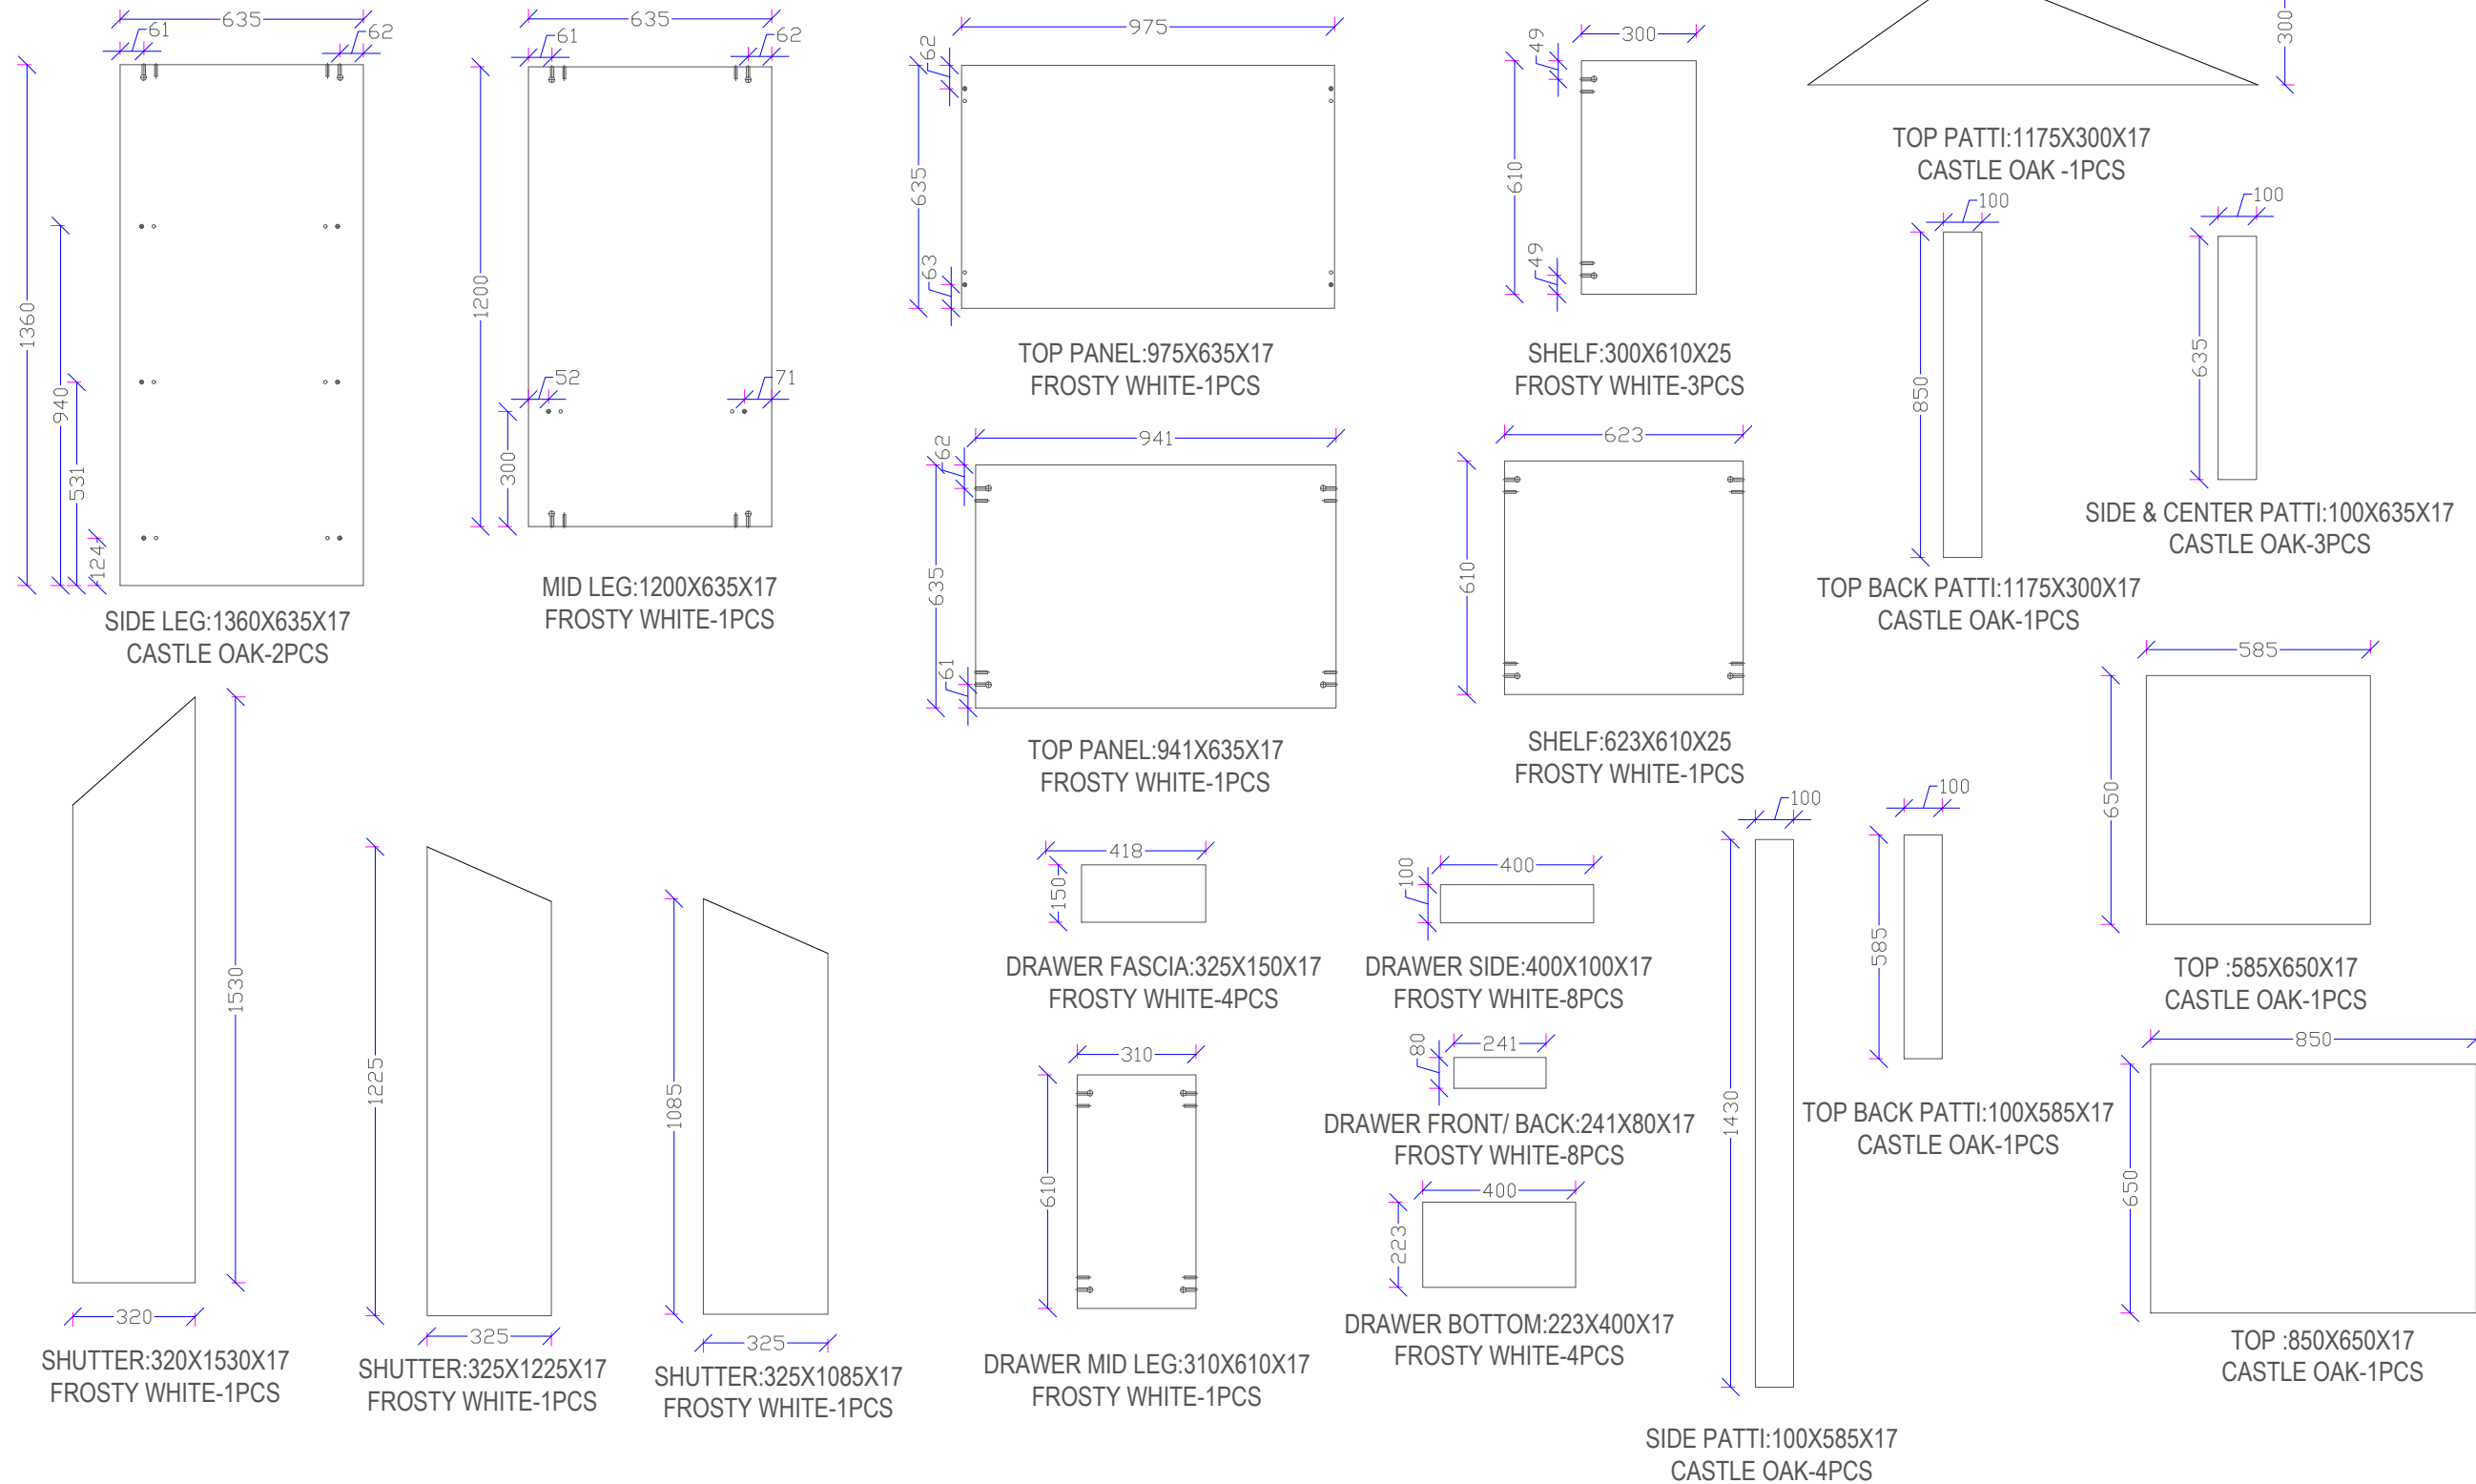

CLIENT:

First issue

rev date notes

REVISIONS:

ISSUED FOR CONSTRUCTION

Resource Consent: N/A

Building Consent: N/A

Tender Issue: N/A

Construction Issue:


PROJECT:



DRAWING TITLE: WARDROBE		
SCALE:	N.T.S.	
DRAWN BY: RANI	CHECKED:	
PRINT DATE: 13/07/2022	PAGE	
PROJECT No.	REVISION	SHEET No.


STUDY TABLE(900X600X1350)
CODE: **FP-ST-21-FO-FW-0.9**

Q3

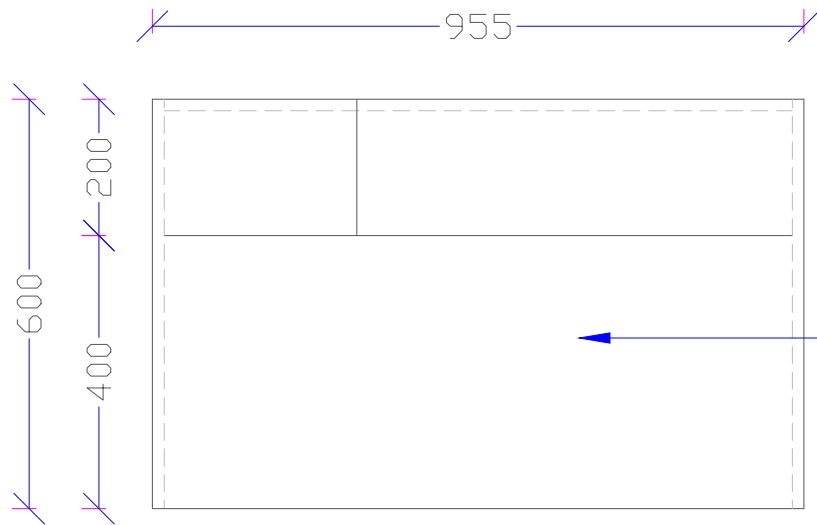

PLAN

TOP PANEL 25MM THK
CASTLE OAK

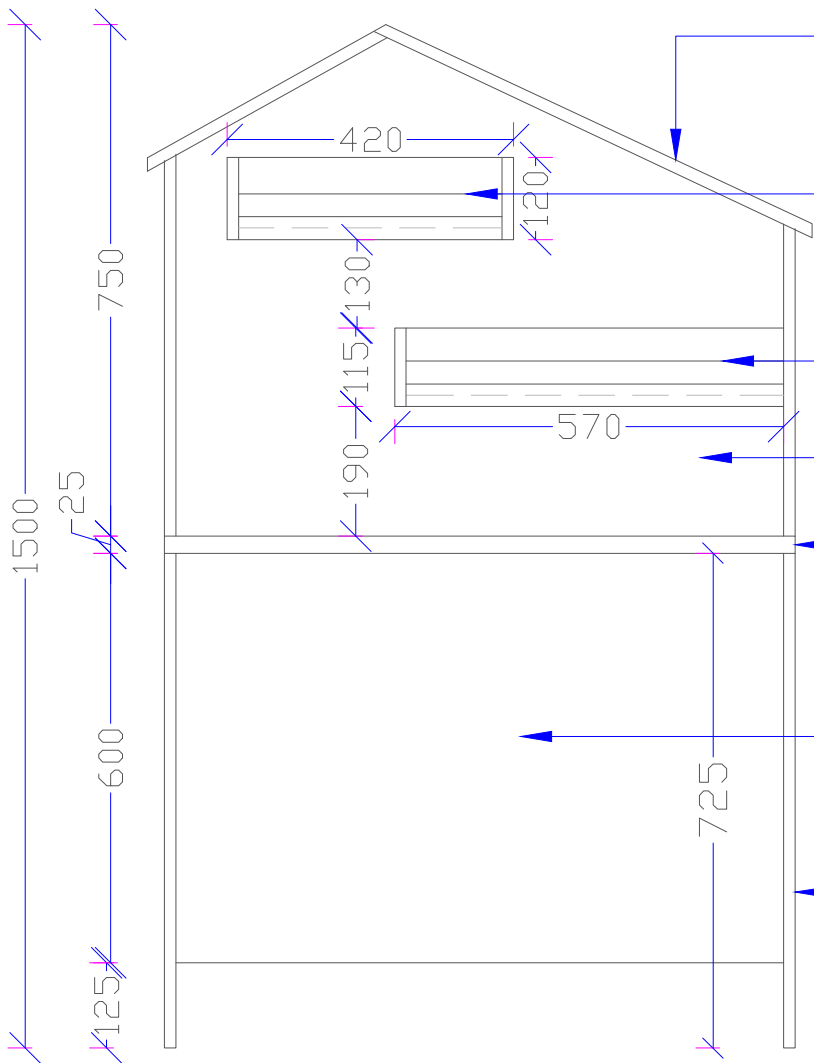

ELEVATION

HUT SHAPE PANEL 17MM
THK CASTLE OAK

SHELF 17MM THK ALL
BLUE DUCO-PAINT

SHELF 17MM THK ALL
GREY DUCO-PAINT

BACK PANEL 17MM
FROSTY WHITE


TOP PANEL 25MM THK
CASTLE OAK

MODESTY 17MM THK
ALL CASTLE OAK

SIDE 17MM THK ALL
CASTLE OAK WITH CUT
OUT IN MIDDLE



REFERENCE IMAGE

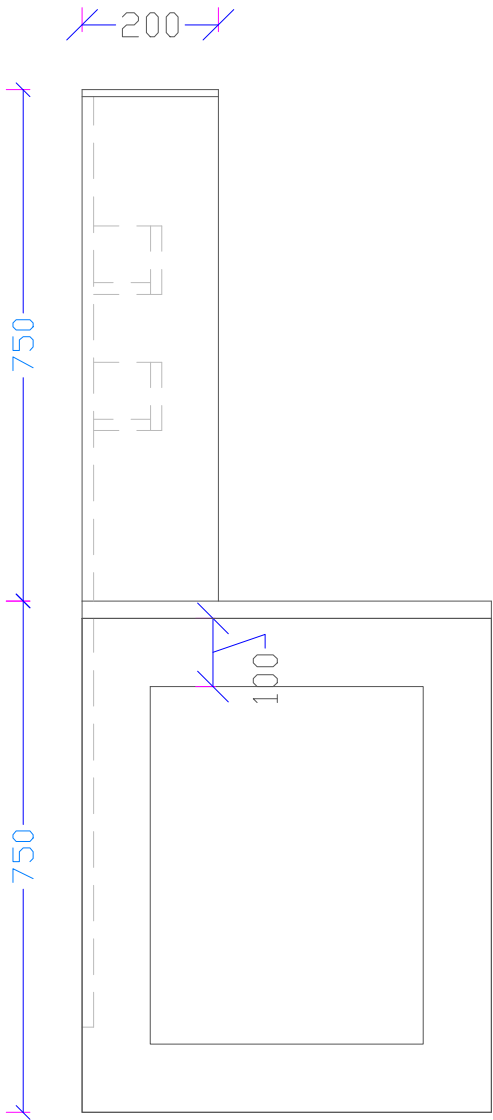

SIDE ELEVATION



SATYA INFRA PROMOTERS PVT. LTD.
KBC-3, THIRD FLOOR, SATYA ARCADE, ALAMBAGH, LUCKNOW, 226005.

General Notes:
Do not scale drawing.
Contractors shall verify all dimensions on site prior to construction.
All work shall be carried out in accordance with local authority regulations.
This drawing is copyright to satya infra promoter pvt ltd
Do not copy drawing without prior consent

NOTE:
1-MINIFIX + DOVEL USED FOR JOINERIES AND
BOARD EDGES ARE TREATED WITH PVC EDGE
BANDING.

CLIENT:

		First issue
rev	date	notes

REVISIONS:

ISSUED FOR CONSTRUCTION

Resource Consent:	N/A
Building Consent:	N/A
Tender Issue:	N/A
Construction Issue:	

PROJECT:



DRAWING TITLE:		
BOOK SHELF		
SCALE: N.T.S.		
DRAWN BY: RANI		CHECKED:
PRINT DATE: 13/07/2022		PAGE
PROJECT No.	REVISION	SHEET No.
	R0	

STUDY TABLE(900X600X1350)
CODE: **FP-ST-21-FO-FW-0.9**

Q3

General Notes:
Do not scale drawing.
Contractors shall verify all dimensions on site prior to construction.
All work shall be carried out in accordance with local authority regulations.
This drawing is copyright to satya infra promoter pvt ltd
Do not copy drawing without prior consent

NOTE:
1-MINIFIX + DOVEL USED FOR JOINERIES AND
BOARD EDGES ARE TREATED WITH PVC EDGE
BANDING.

CLIENT:


		First Issue
rev	date	notes

REVISIONS:

ISSUED FOR CONSTRUCTION
Resource Consent: N/A
Building Consent: N/A
Tender Issue: N/A
Construction Issue:


PROJECT:

DRAWING TITLE: BOOK SHELF		
SCALE: N.T.S.		
DRAWN BY: RANI		CHECKED:
PRINT DATE: 13/07/2022	PAGE	
PROJECT No.	REVISION	SHEET No.
	R0	

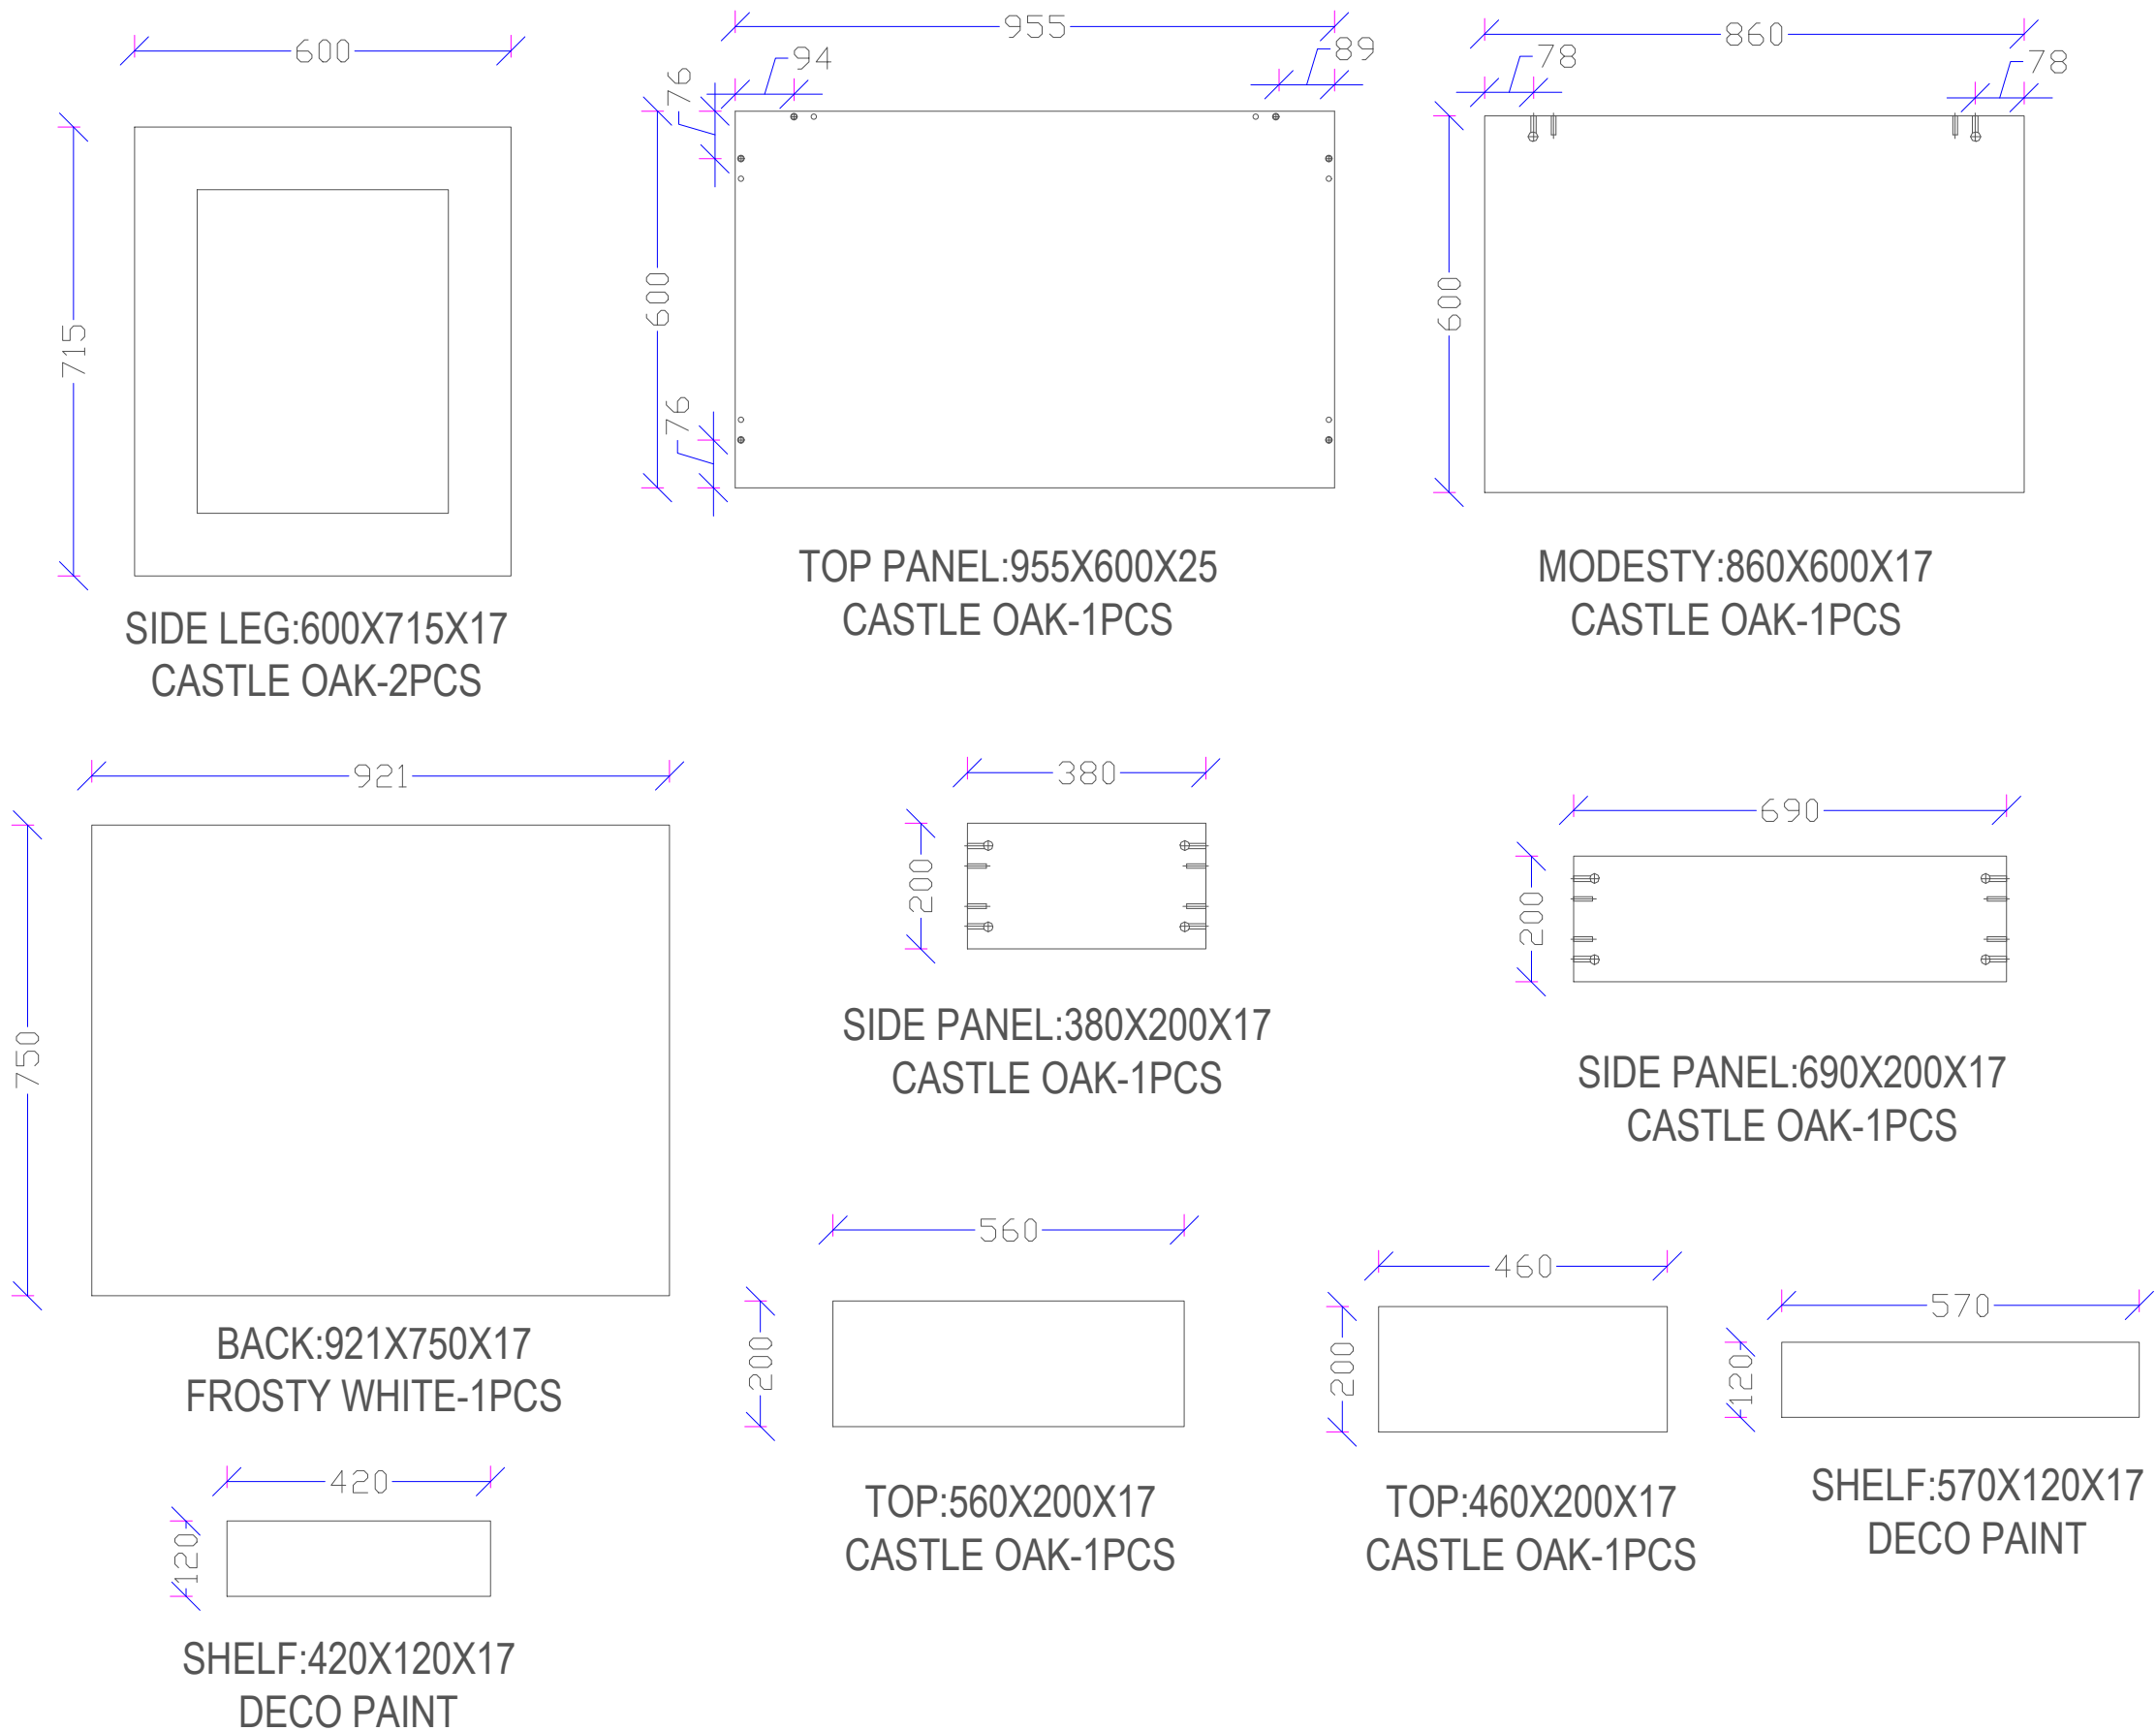


BOOK SHELF (450X450X1530)
CODE: **FP-BS-1-FO-FW-0.45**

Q4

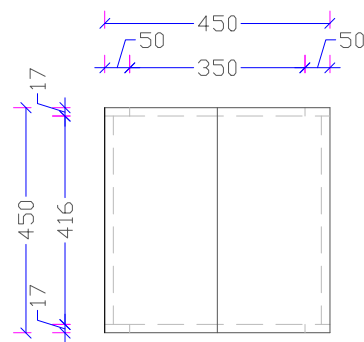


PLAN

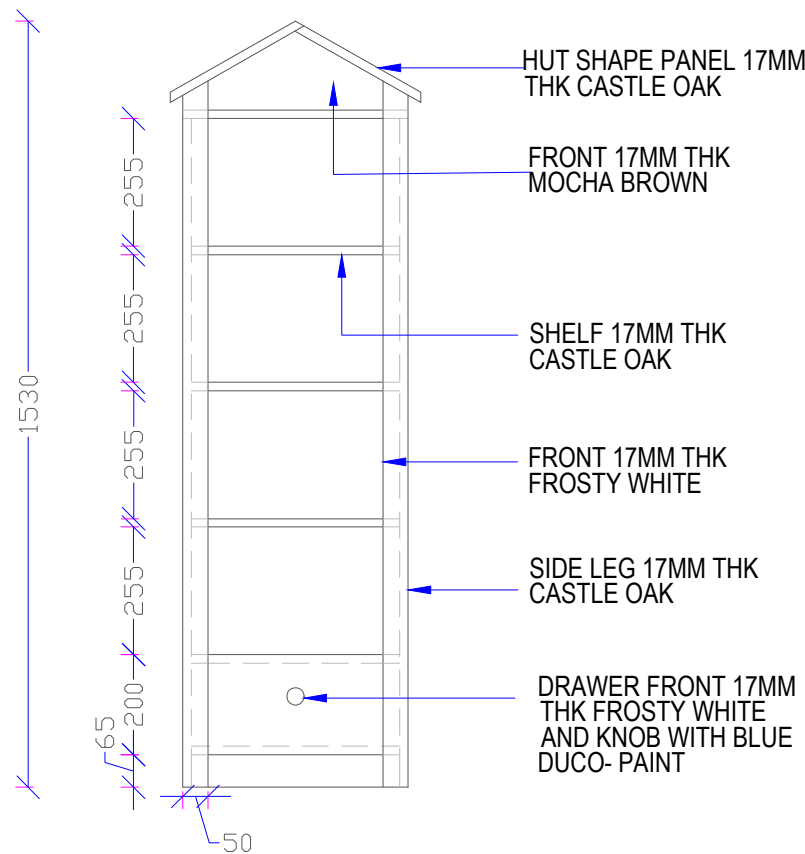


ELEVATION

DISPLAY SHELF (375X450X955)
CODE: **FP-BS-02-FO-FW-0.35**

Q5

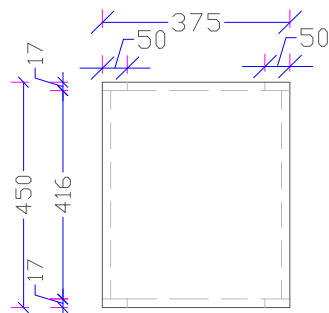

PLAN

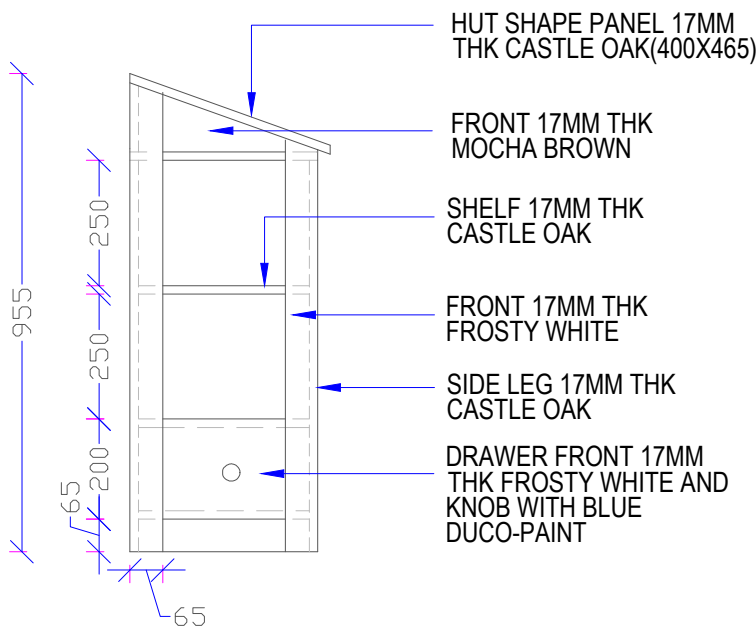

ELEVATION



REFERENCE IMAGE



SATYA INFRA PROMOTERS PVT. LTD.
KBC-3, THIRD FLOOR, SATYA ARCADE, ALAMBAGH, LUCKNOW, 226005.

General Notes:
Do not scale drawing.
Contractors shall verify all dimensions on site prior to construction.
All work shall be carried out in accordance with local authority regulations.
This drawing is copyright to satya infra promoter pvt ltd
Do not copy drawing without prior consent

NOTE:
1-MINIFIX + DOVEL USED FOR JOINERIES AND
BOARD EDGES ARE TREATED WITH PVC EDGE
BANDING.

CLIENT:

rev	date	notes
		First Issue

REVISIONS:

ISSUED FOR CONSTRUCTION

Resource Consent: N/A

Building Consent: N/A

Tender Issue: N/A

Construction Issue:


PROJECT:



DRAWING TITLE: BOOK SHELF		
SCALE: N.T.S.		
DRAWN BY: RANI		CHECKED:
PRINT DATE: 13/07/2022		PAGE
PROJECT No.	REVISION	SHEET No.
	R0	

BOOK SHELF (450X450X1530)
CODE: **FP-BS-1-FO-FW-0.45**

Q4

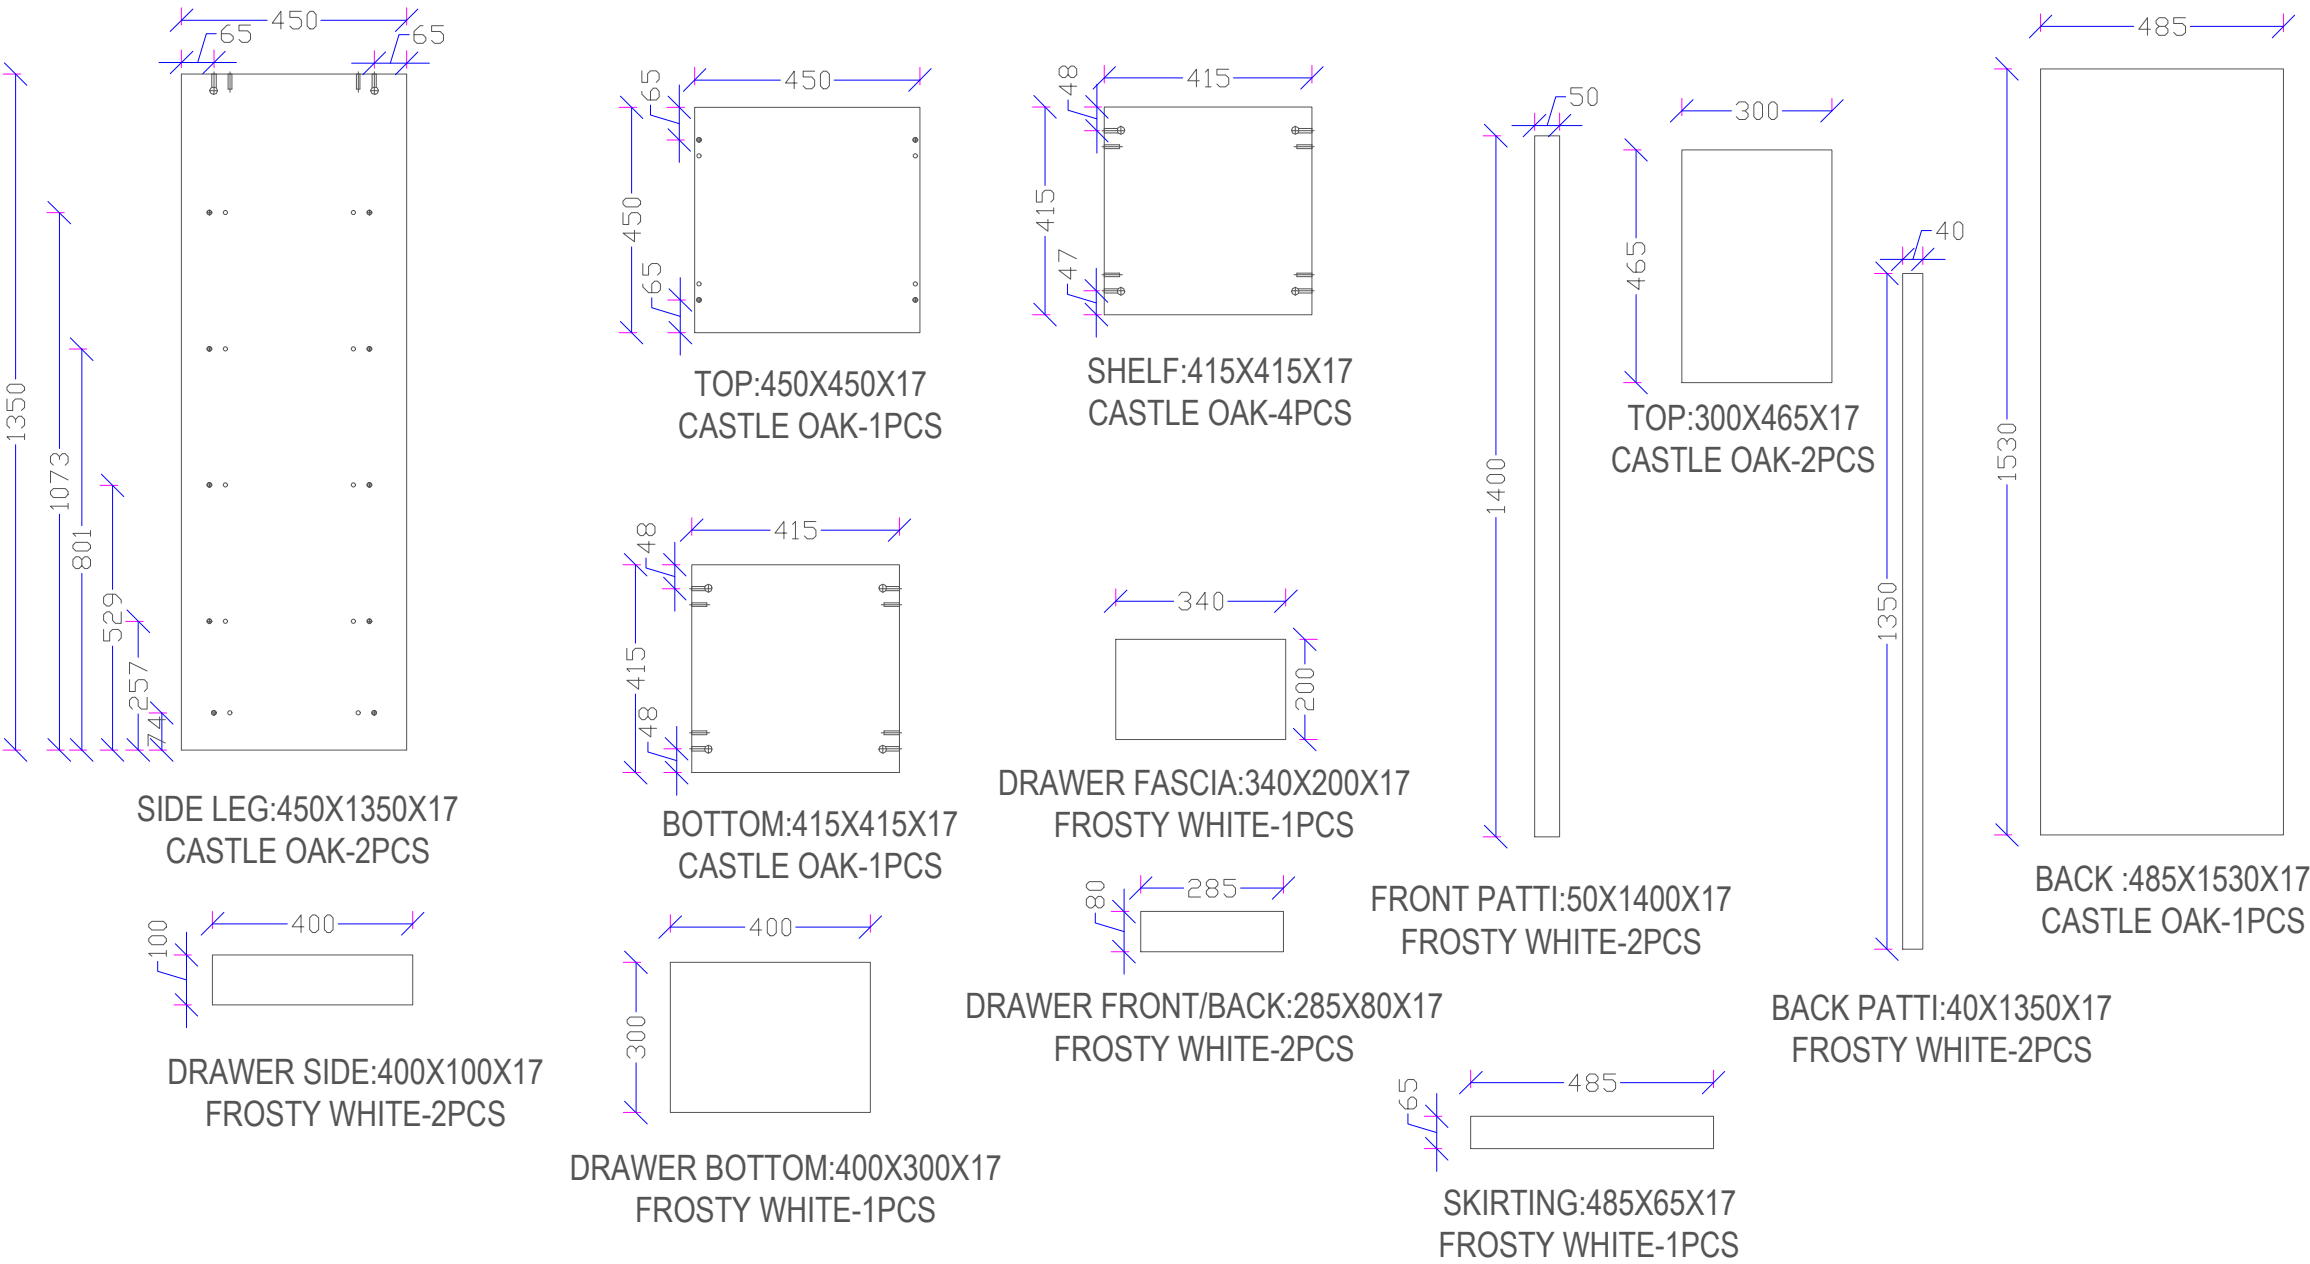

General Notes:
Do not scale drawing.
Contractors shall verify all dimensions on site prior to construction.
All work shall be carried out in accordance with local authority regulations.
This drawing is copyright to satya infra promoter pvt ltd
Do not copy drawing without prior consent

NOTE:
1-MINIFIX + DOVEL USED FOR JOINERIES AND
BOARD EDGES ARE TREATED WITH PVC EDGE
BANDING.

CLIENT:

		First Issue
rev	date	notes

REVISIONS:


ISSUED FOR CONSTRUCTION
Resource Consent: N/A
Building Consent: N/A
Tender Issue: N/A
Construction Issue:

PROJECT:

DRAWING TITLE: BOOK SHELF		
SCALE: N.T.S.		
DRAWN BY: RANI		CHECKED:
PRINT DATE: 13/07/2022	PAGE	
PROJECT No.	REVISION	SHEET No.
	R0	

DISPLAY SHELF (375X450X955)
CODE:FP-BS-02-FO-FW-0.35

Q5

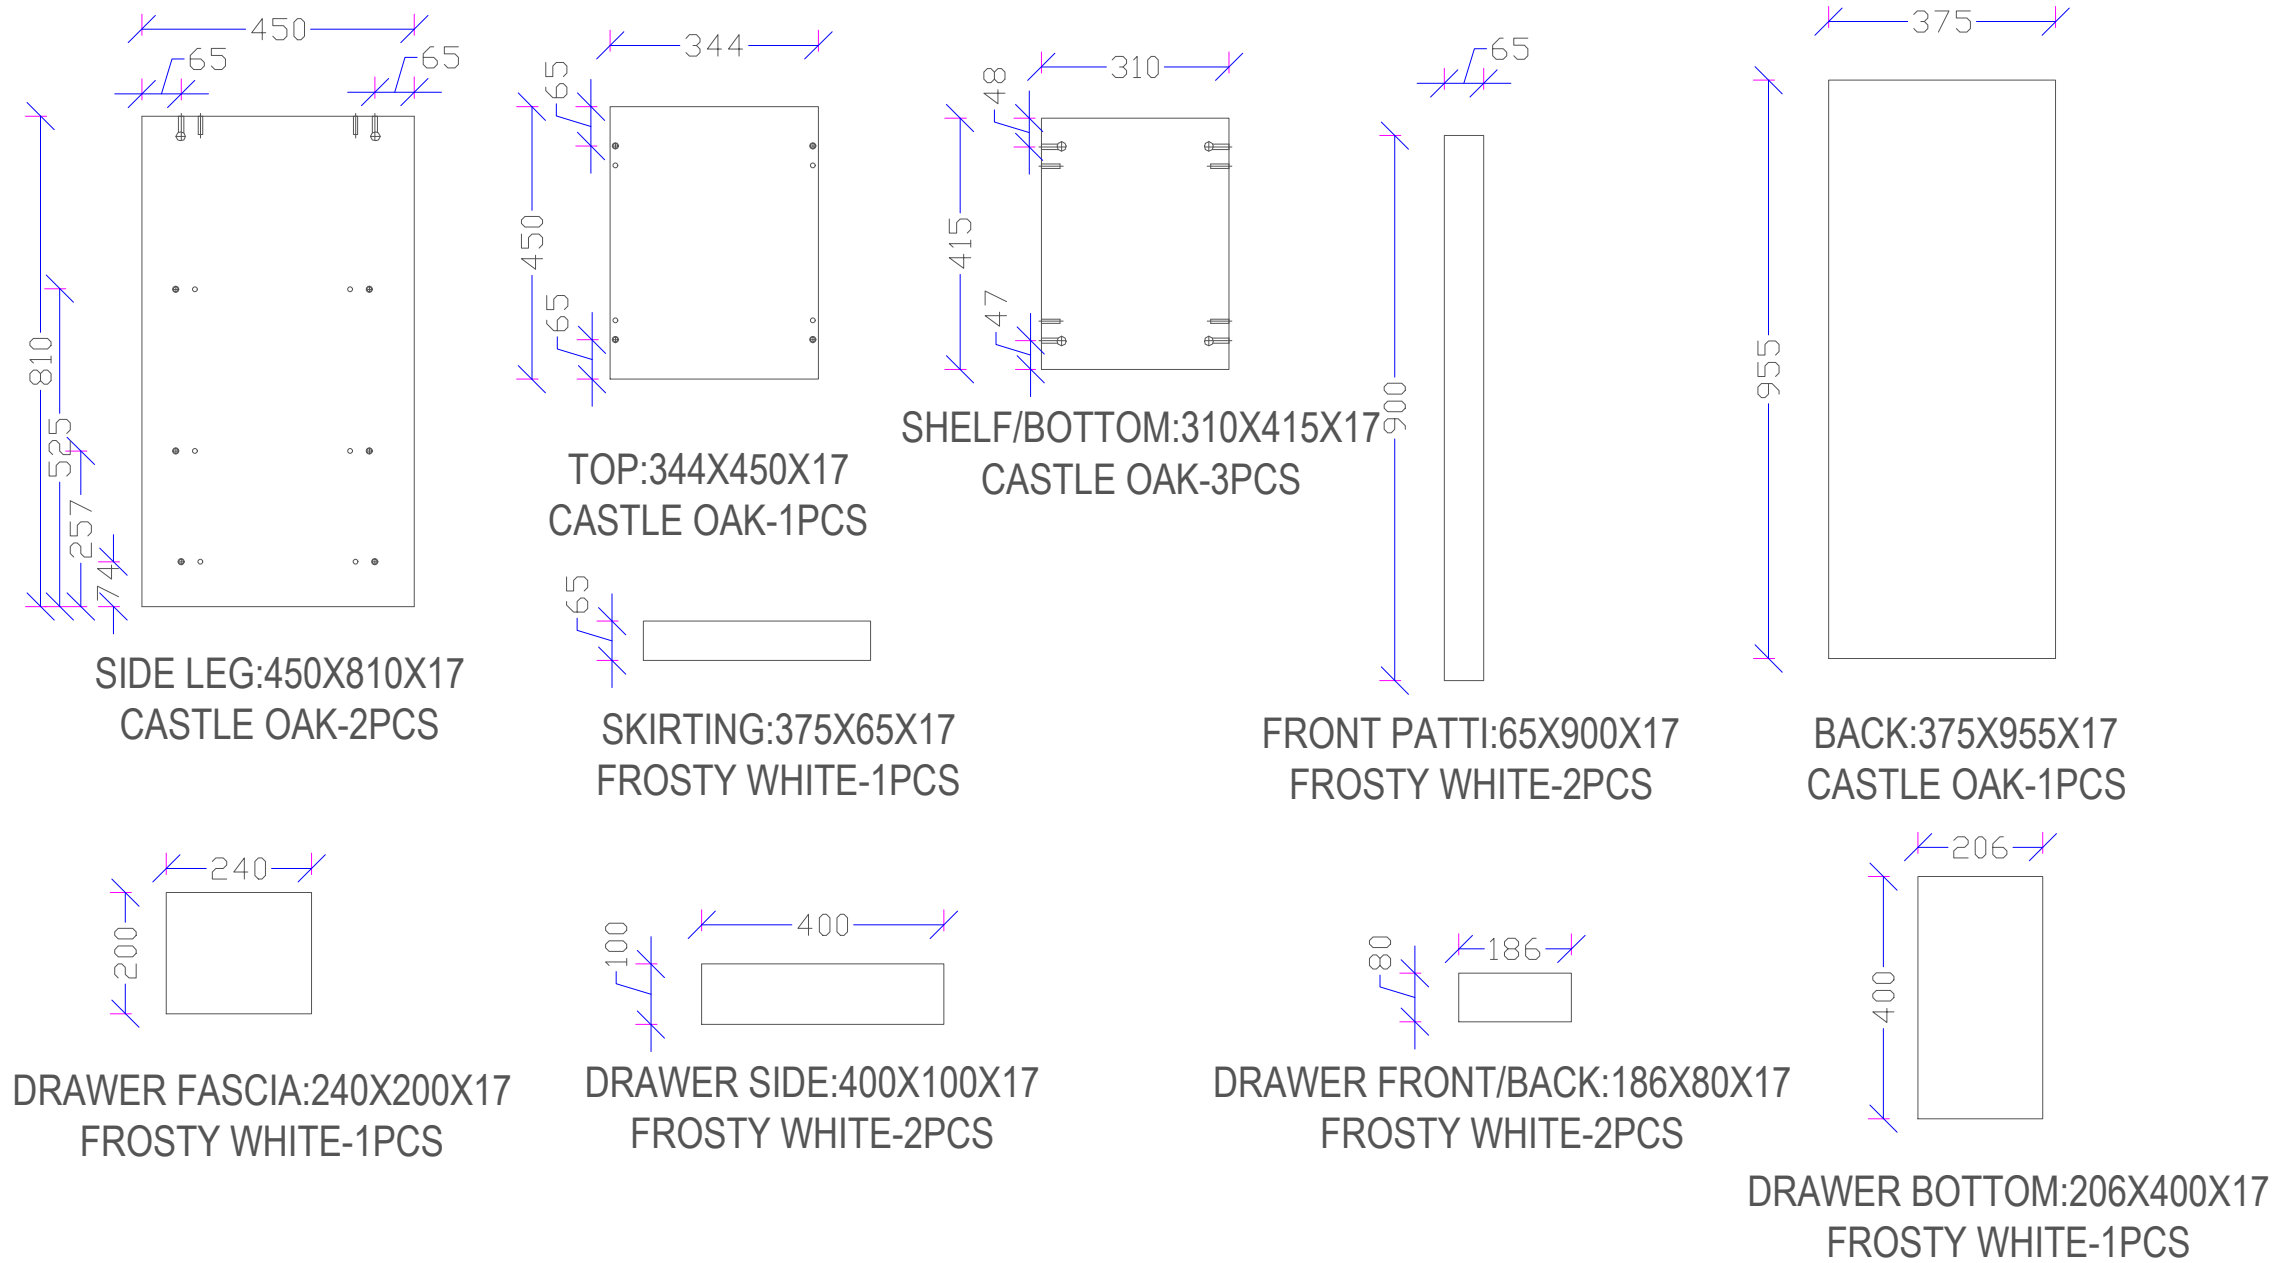

General Notes:
Do not scale drawing.
Contractors shall verify all dimensions on site prior to construction.
All work shall be carried out in accordance with local authority regulations.
This drawing is copyright to satya infra promoter pvt ltd
Do not copy drawing without prior consent

NOTE:
1-MINIFIX + DOVEL USED FOR JOINERIES AND
BOARD EDGES ARE TREATED WITH PVC EDGE
BANDING.

CLIENT:

		First Issue
rev	date	notes

REVISIONS:

ISSUED FOR CONSTRUCTION
Resource Consent: N/A
Building Consent: N/A
Tender Issue: N/A
Construction Issue:

PROJECT:

DRAWING TITLE: BOOK SHELF		
SCALE: N.T.S.		
DRAWN BY: RANI		CHECKED:
PRINT DATE: 13/07/2022		PAGE
PROJECT No.	REVISION	SHEET No.
	R0	