


KITCHEN (1725X600X2140)
CODE:FP-K-50-CP-W-1.75

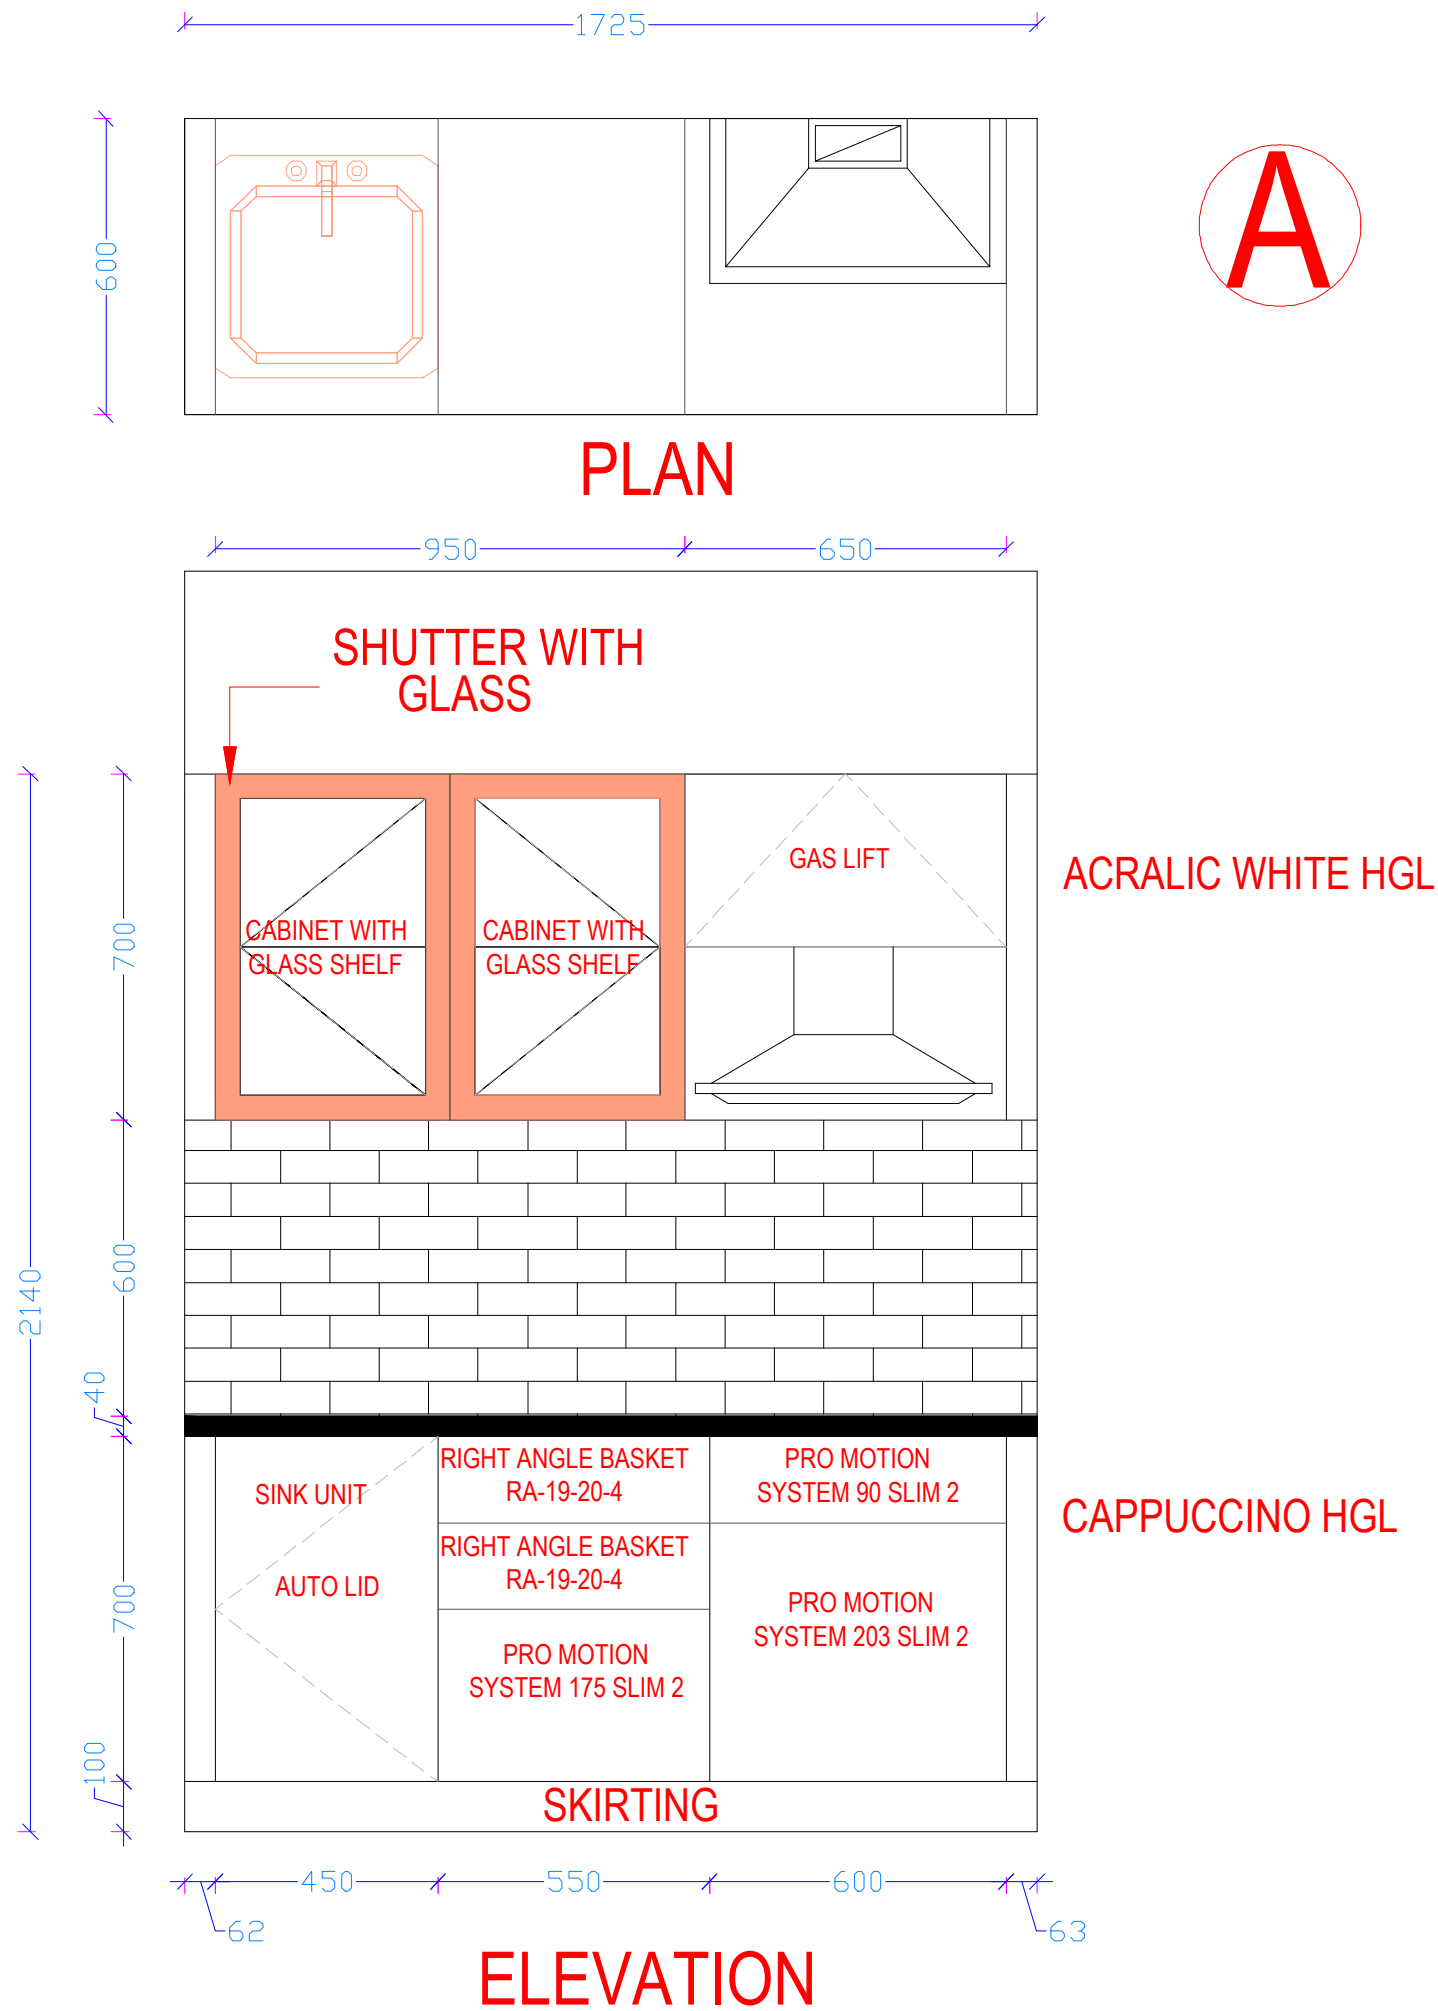

General Notes:
Do not scale drawing.
Contractors shall verify all dimensions on site prior to construction.
All work shall be carried out in accordance with local authority regulations.
This drawing is copyright to satya infra promoter pvt ltd
Do not copy drawing without prior consent

NOTE:
1-MINIFIX + DOVEL USED FOR JOINERIES AND BOARD EDGES ARE TREATED WITH PVC EDGE BANDING.

CLIENT:

rev	date	notes
		First Issue

REVISIONS:

ISSUED FOR CONSTRUCTION
Resource Consent: N/A
Building Consent: N/A
Tender Issue: N/A
Construction Issue:

PROJECT:

DRAWING TITLE:
KITCHEN

SCALE:	N.T.S.
DRAWN BY: RANI	CHECKED:
PRINT DATE: 13/07/2022	PAGE
PROJECT No.	REVISION SHEET No.
	R0